


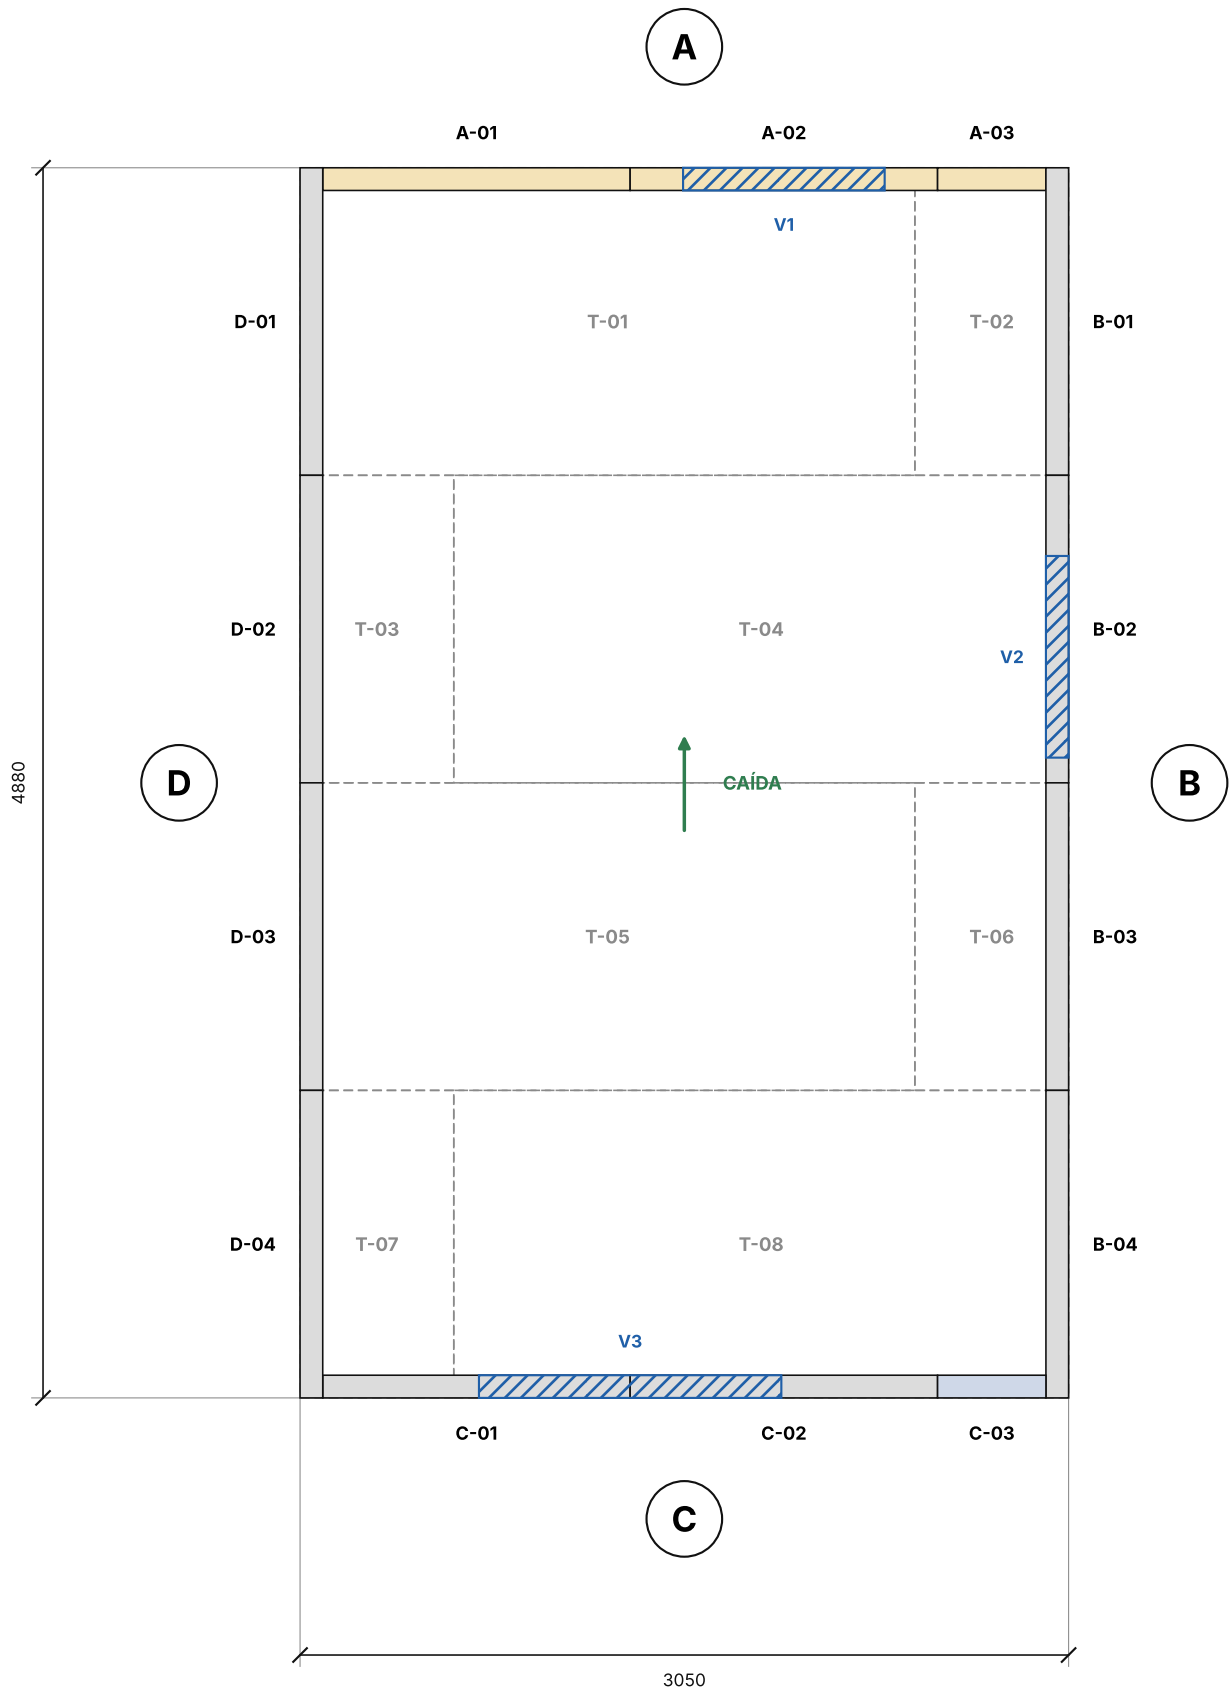

PANELES (medidas en mm)

Cód.	Ancho	Alto	Observaciones
A-01	1220	2220	smart
A-02	1220	2220	smart · vanos V1
A-03	430	2220	ajuste · smart
B-01	1220	2440	
B-02	1220	2440	vanos V2
B-03	1220	2440	
B-04	1220	2440	
C-01	1220	2440	vanos V3
C-02	1220	2440	vanos V3
C-03	430	2440	ajuste
D-01	1220	2440	
D-02	1220	2440	
D-03	1220	2440	
D-04	1220	2440	
T-01	2440	1220	techo
T-02	610	1220	techo ajuste
T-03	610	1220	techo ajuste
T-04	2440	1220	techo
T-05	2440	1220	techo
T-06	610	1220	techo ajuste
T-07	610	1220	techo ajuste
T-08	2440	1220	techo

RESUMEN

Paneles de muro: 14 · Paneles de techo: 8
Caída hacia el lado A (muro bajo 2220 mm, el resto 2440 mm)

ALERTAS (1)

- B-02: V2 a 10.0 cm del borde derecho (mínimo 20.0 cm).

REFERENCIAS

- Panel SIP
- Pieza de ajuste
- Con smart panel
- Vano

Lados vistos en planta: A arriba, B derecha, C abajo, D izquierda.
Numeración: A y C de izquierda a derecha; B y D de arriba hacia abajo.