


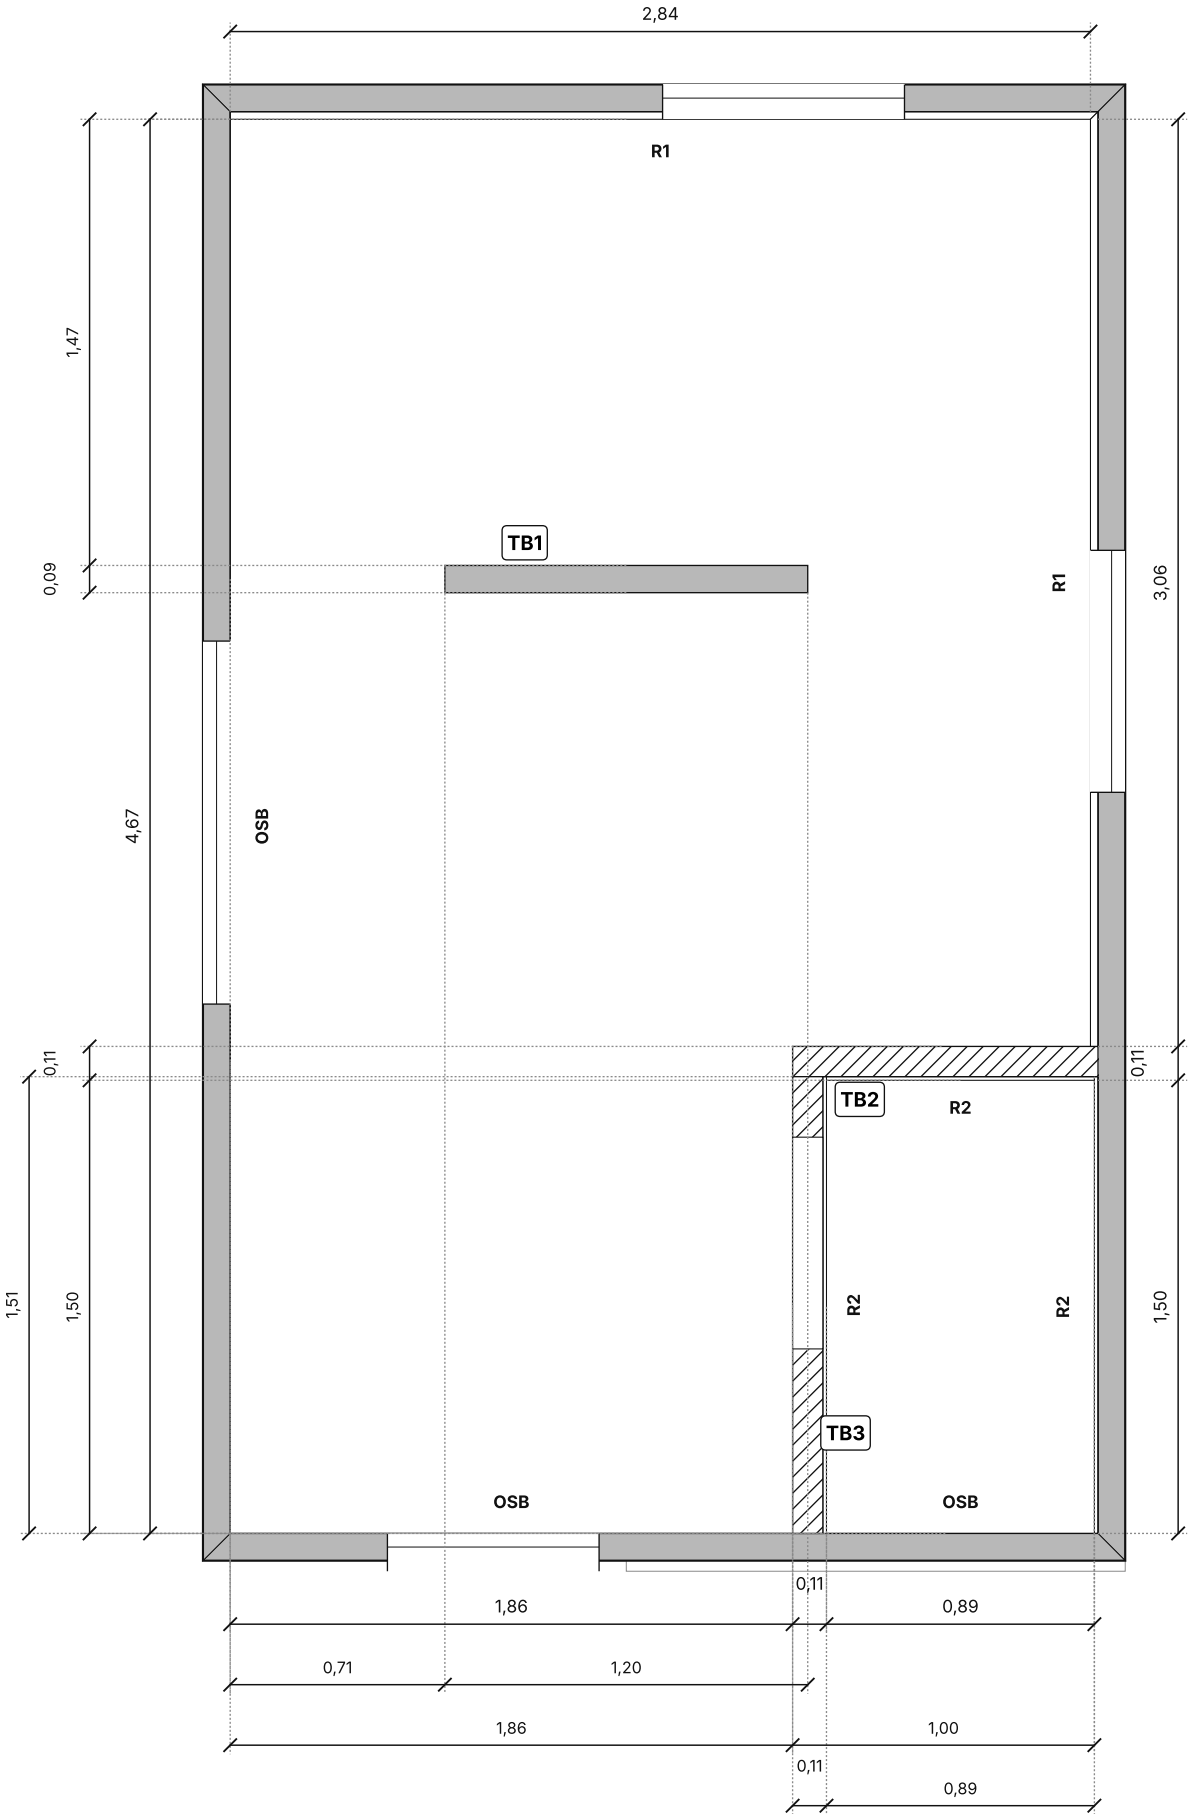

REVESTIMIENTOS INTERIORES

R1 Placa de yeso s/ omega (2,50 cm)
R2 Cerámico pegado (1,20 cm)
OSB: OSB del SIP visto (sin revestimiento).
DL: placa del tabique de durlock, sin revestimiento agregado.


TABIQUES

TB1 SIP · espesor 0,09 terminado (0,09 de obra) · largo 1,20
TB2 Durlock · espesor 0,11 terminado (0,10 de obra) · largo 1,00
TB3 Durlock · espesor 0,11 terminado (0,10 de obra) · largo 1,51

- SIP (muros y tabiques)
- Tabique de durlock

NOTAS

Cotas al revestimiento terminado; donde no hay revestimiento, al SIP o a la placa del tabique.
Por fuera de cada muro: cadena medida sobre su cara interior terminada (esquinas, cambios de revestimiento y caras terminadas de los tabiques que llegan).
Más afuera, abajo y a la izquierda: una cadena por tabique, de través (sus caras terminadas) y a lo largo (sus extremos), desde la cara terminada más cercana. Todas las cotas van por fuera del dibujo, con líneas guía de puntos.
El código de cada tramo va del lado del local. Ver alturas y bocas en las vistas interiores.

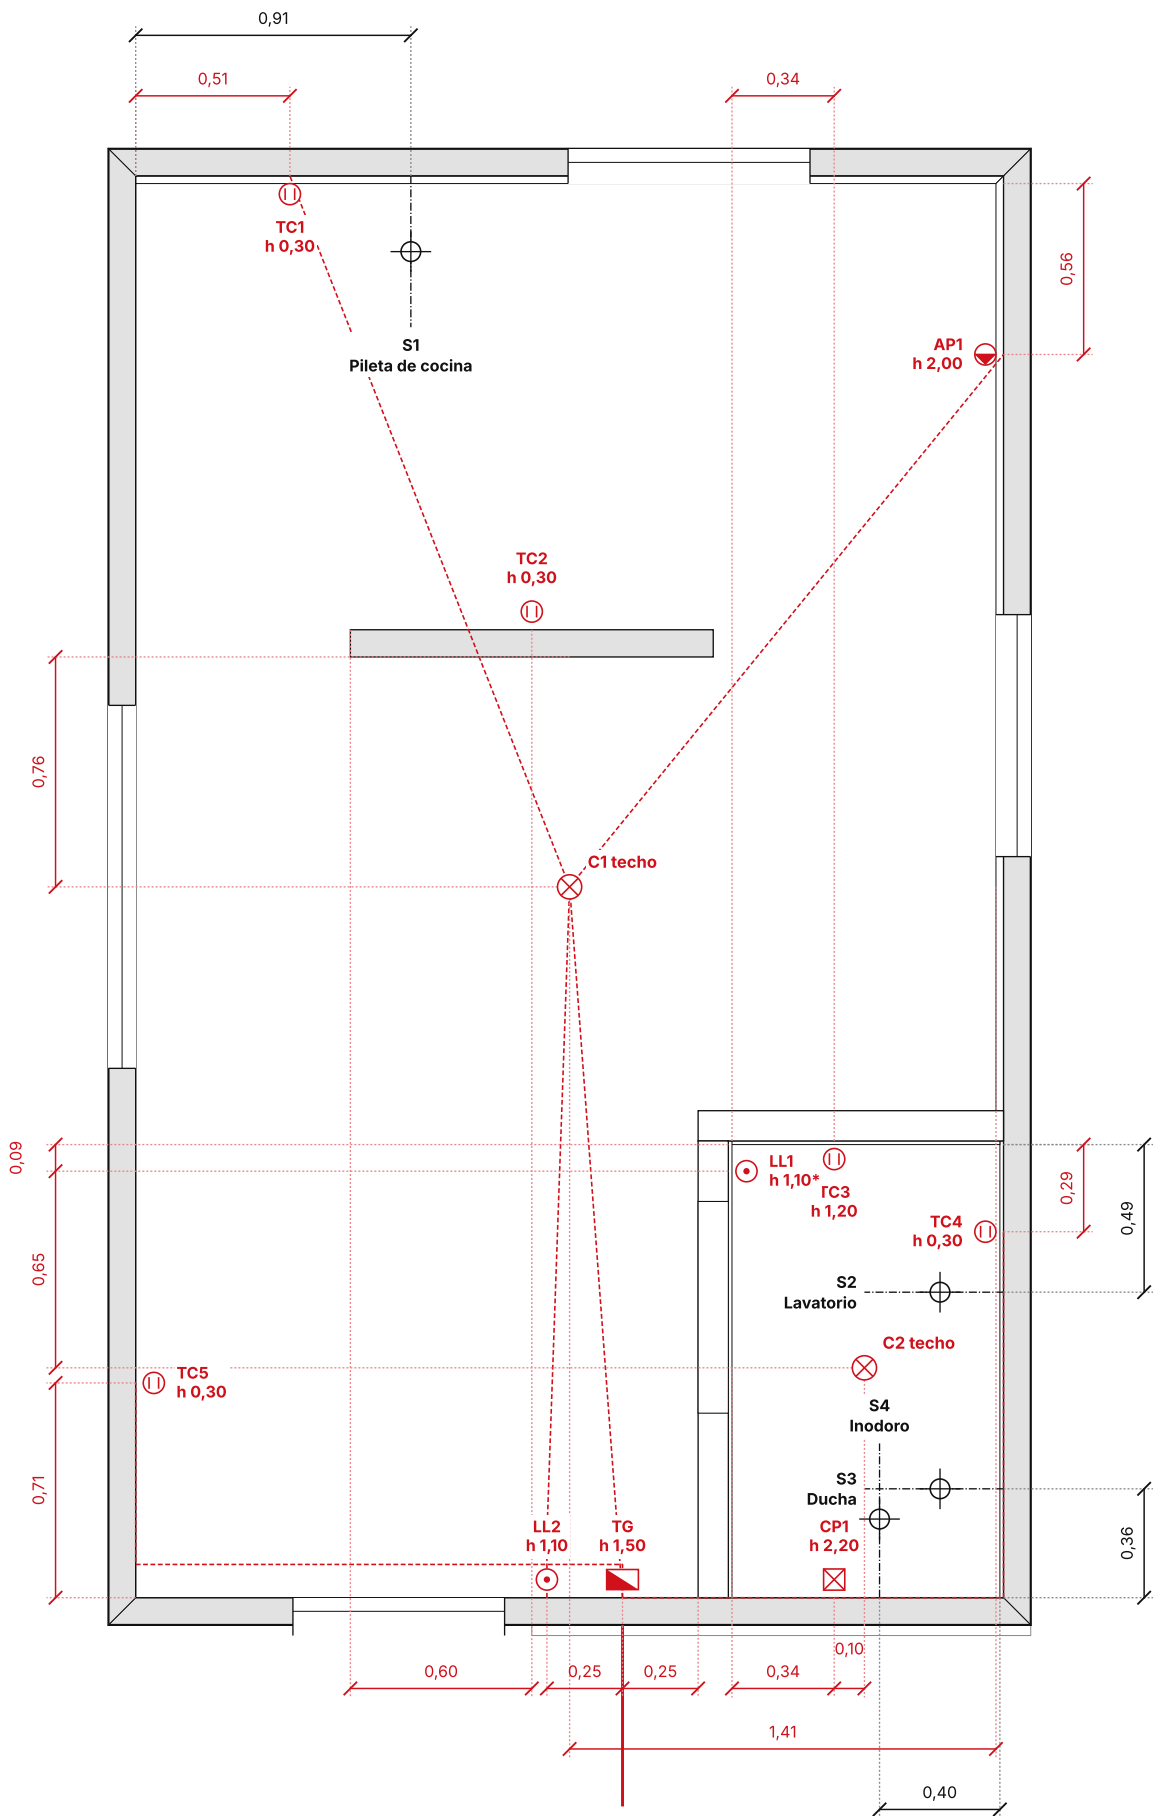

REFERENCIAS

- TG Tablero (h típica 1,50)
- TC Tomacorriente (h típica 0,30)
- LL Llave de efecto (h típica 1,10)
- AP Aplique de pared (h típica 2,00)
- CP Caja de pase (h típica 2,20)
- C Boca de techo (centro)
- Cañería embutida (solo esquema)
- Cañería vista sobre el módulo
- S Eje de artefacto sanitario

BOCAS Y EJES (código · altura · cara)

- TC1 h 0,30 A
- AP1 h 2,00 B
- TC2 h 0,30 TB1-A
- C1 h techo techo
- TC3 h 1,20 TB2-C
- LL1 h 1,10* TB3-B
- TC4 h 0,30 B
- C2 h techo techo
- TC5 h 0,30 D
- LL2 h 1,10 C
- TG h 1,50 C
- CP1 h 2,20 C
- S1 Pileta de cocina · A
- S2 Lavatorio · B
- S3 Ducha · B
- S4 Inodoro · C


NOTAS

Cotas por fuera del dibujo, a eje de cada caja o artefacto, desde las caras terminadas (revestimiento, o SIP si no hay), desde la cara terminada más cercana sobre la que va (esquina o tabique). Cada boca se acota del lado hacia el que mira su cara; las de techo, en x abajo y en y a la izquierda. En rojo, electricidad.


h: altura del eje de la caja desde el piso (base del panel).

Las cañerías van solo dibujadas: se ajustan en obra.


* Altura típica: el bloque no trae el atributo ALTURA.

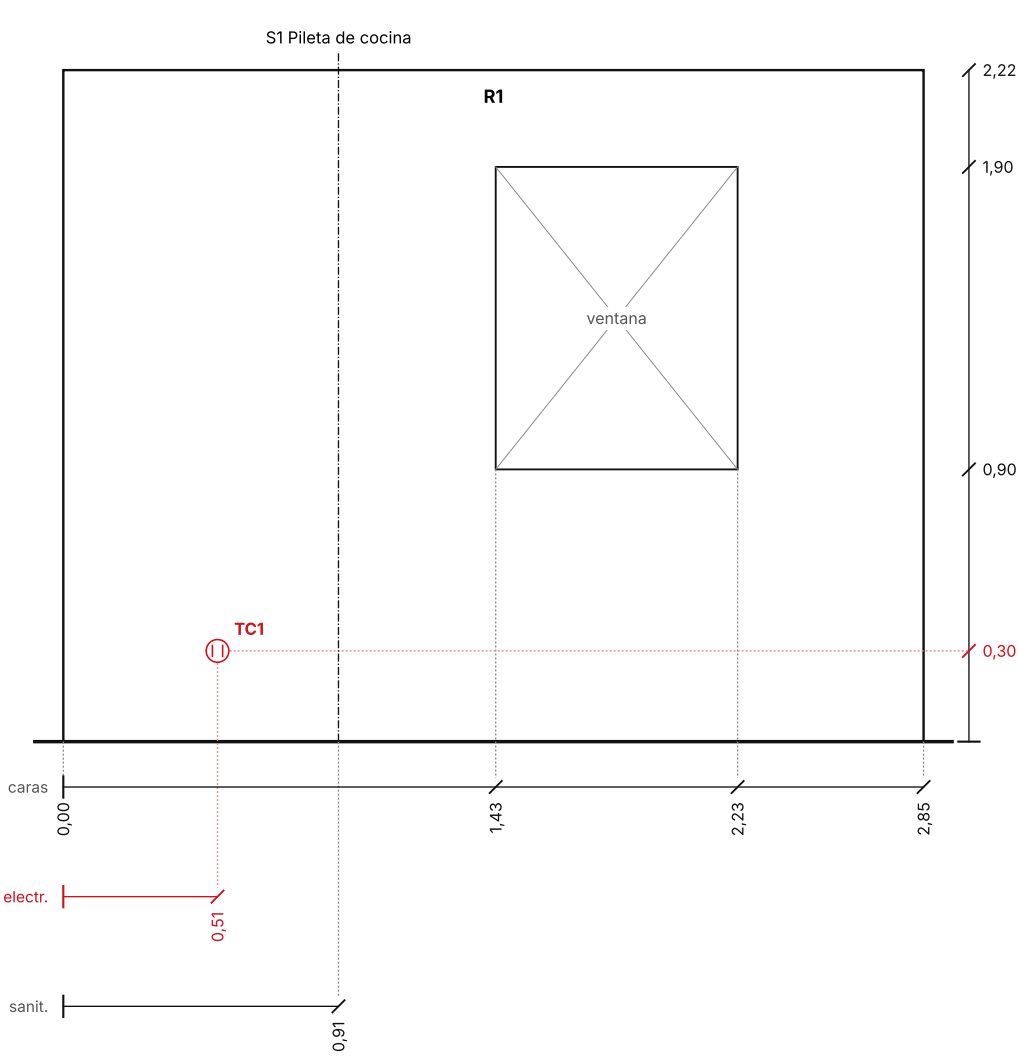


MURO A
Vista desde el interior

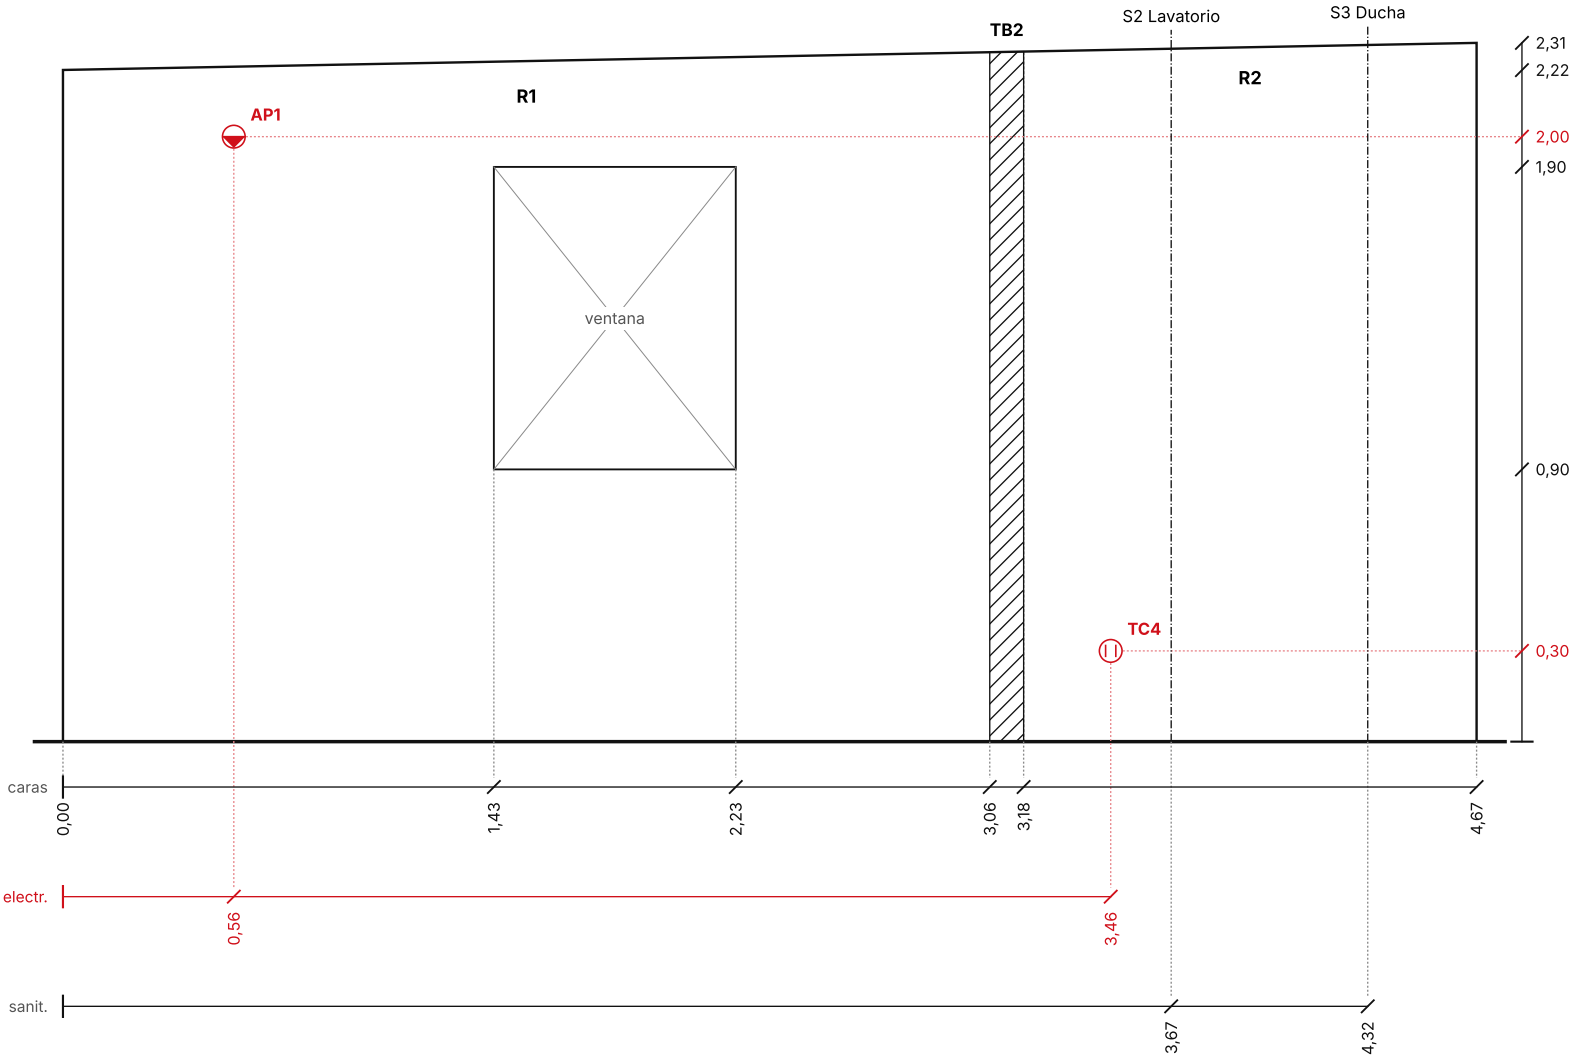


MURO B
Vista desde el interior

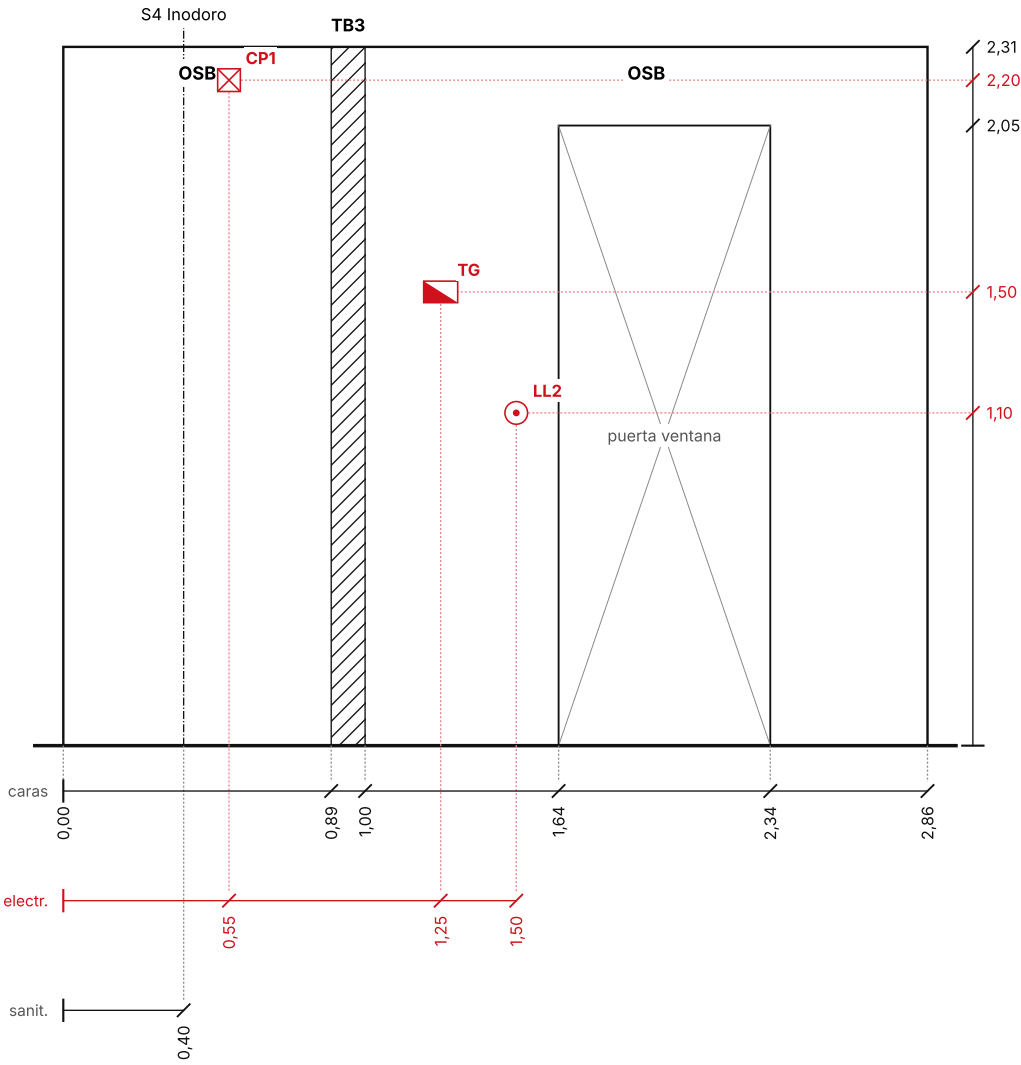

MURO C
Vista desde el interior

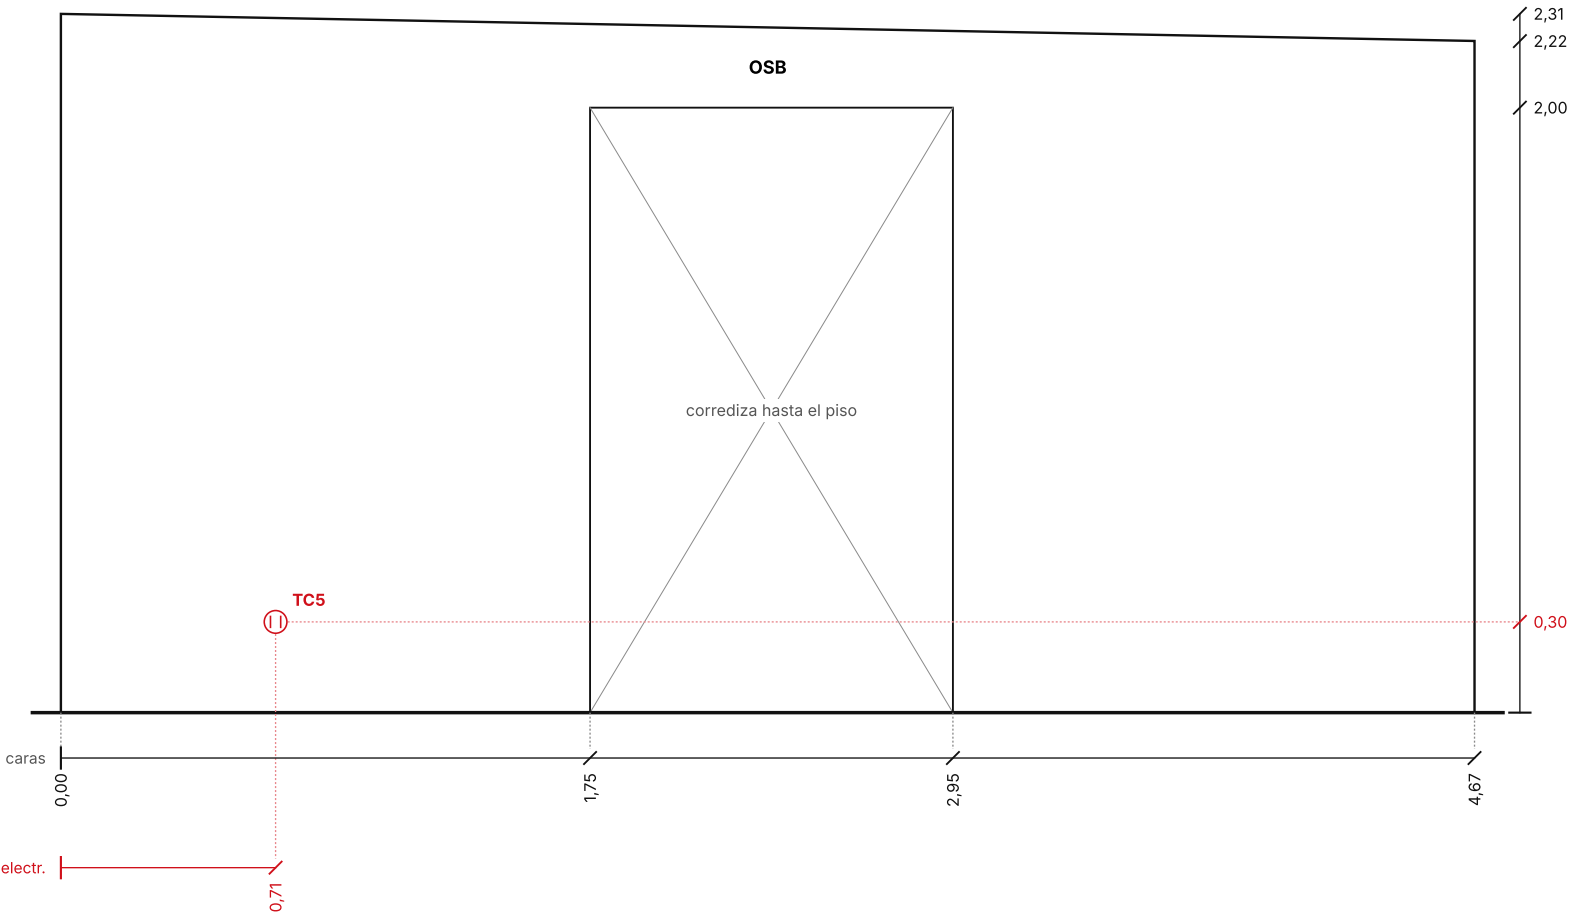


MURO D
Vista desde el interior

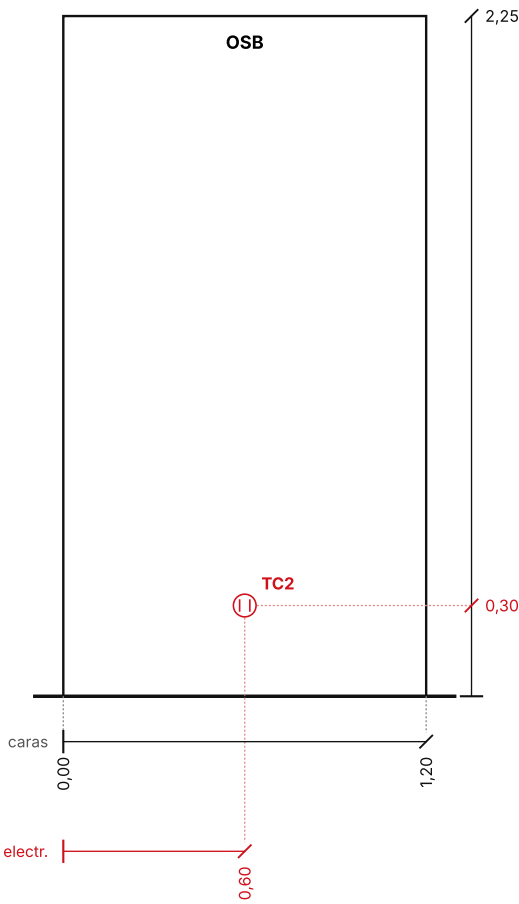


TABIQUE TB1 · CARA HACIA A

Vista desde el interior

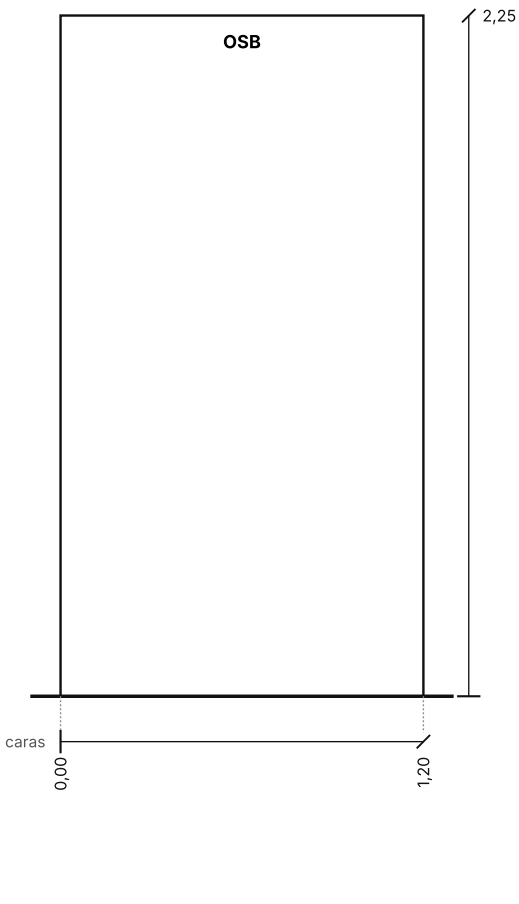


TABIQUE TB1 · CARA HACIA C

Vista desde el interior

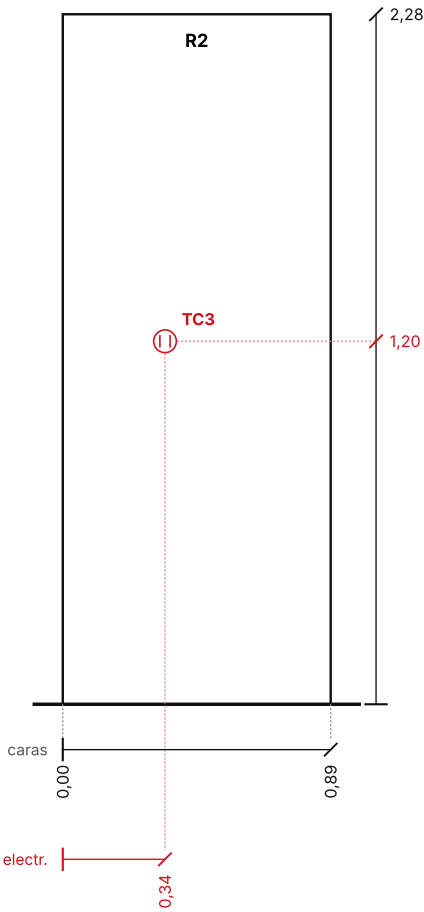


TABIQUE TB2 · CARA HACIA C

Vista desde el interior

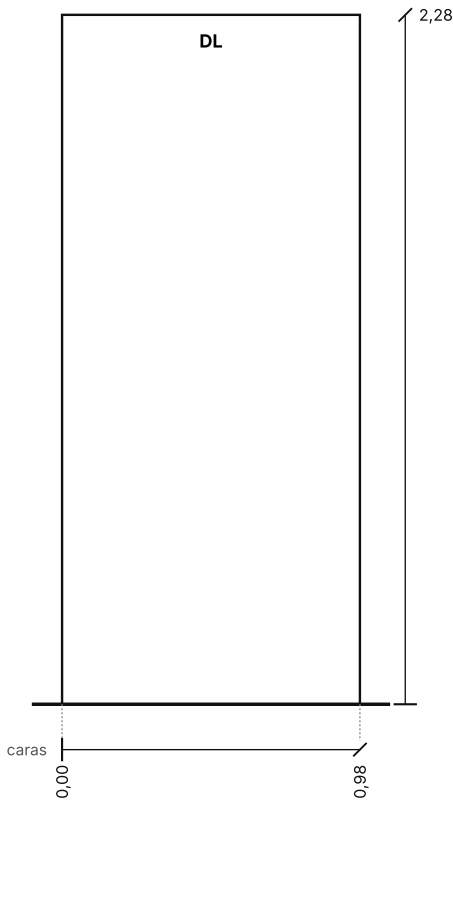


TABIQUE TB2 · CARA HACIA A

Vista desde el interior

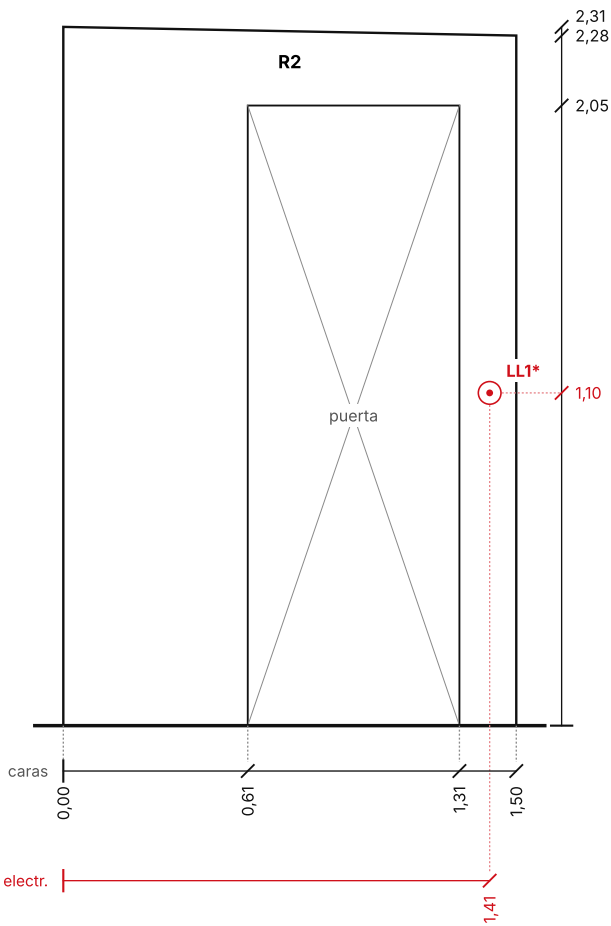

TABIQUE TB3 · CARA HACIA B

Vista desde el interior

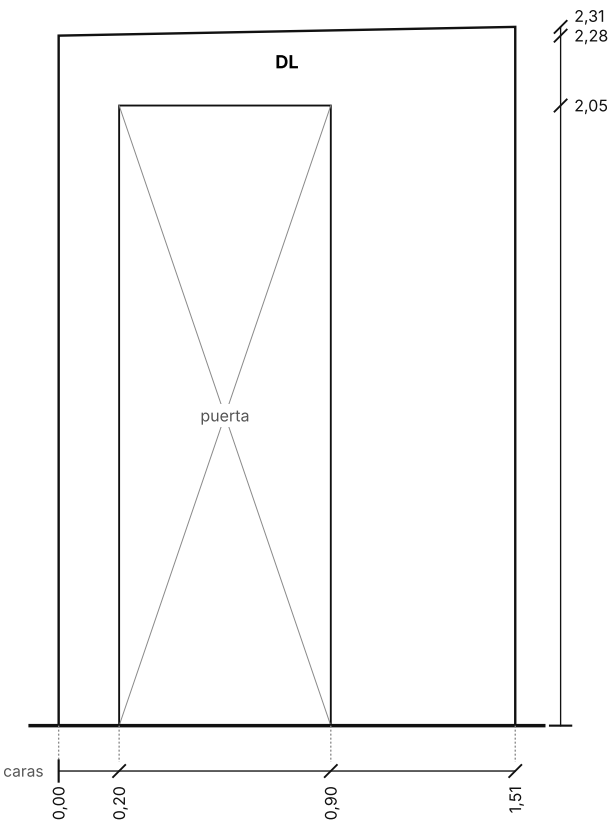

TABIQUE TB3 · CARA HACIA D

Vista desde el interior